**TK-101 FEED TANK**
CAP: 50 m3
SIZE: 3600 ID x 5000 H
DP/DT: ATM / 60 C
MOC: CS

**P-101A/B FEED PUMP**
CAP: 30 m3/h x 45 m
MOTOR: 11 kW
TYPE: CENTRIFUGAL
MOC: CS/SS316

**E-101 FEED PREHEATER**
DUTY: 450 kW
TYPE: SHELL & TUBE (BEM)
DP: 10 / 6 barg
MOC: CS / SS304

**V-101 FLASH SEPARATOR**
SIZE: 1500 ID x 4000 T/T
DP/DT: 8 barg / 150 C
MOC: CS

**TK-102 SLOP TANK**
CAP: 10 m3
DP/DT: ATM / 60 C
MOC: CS

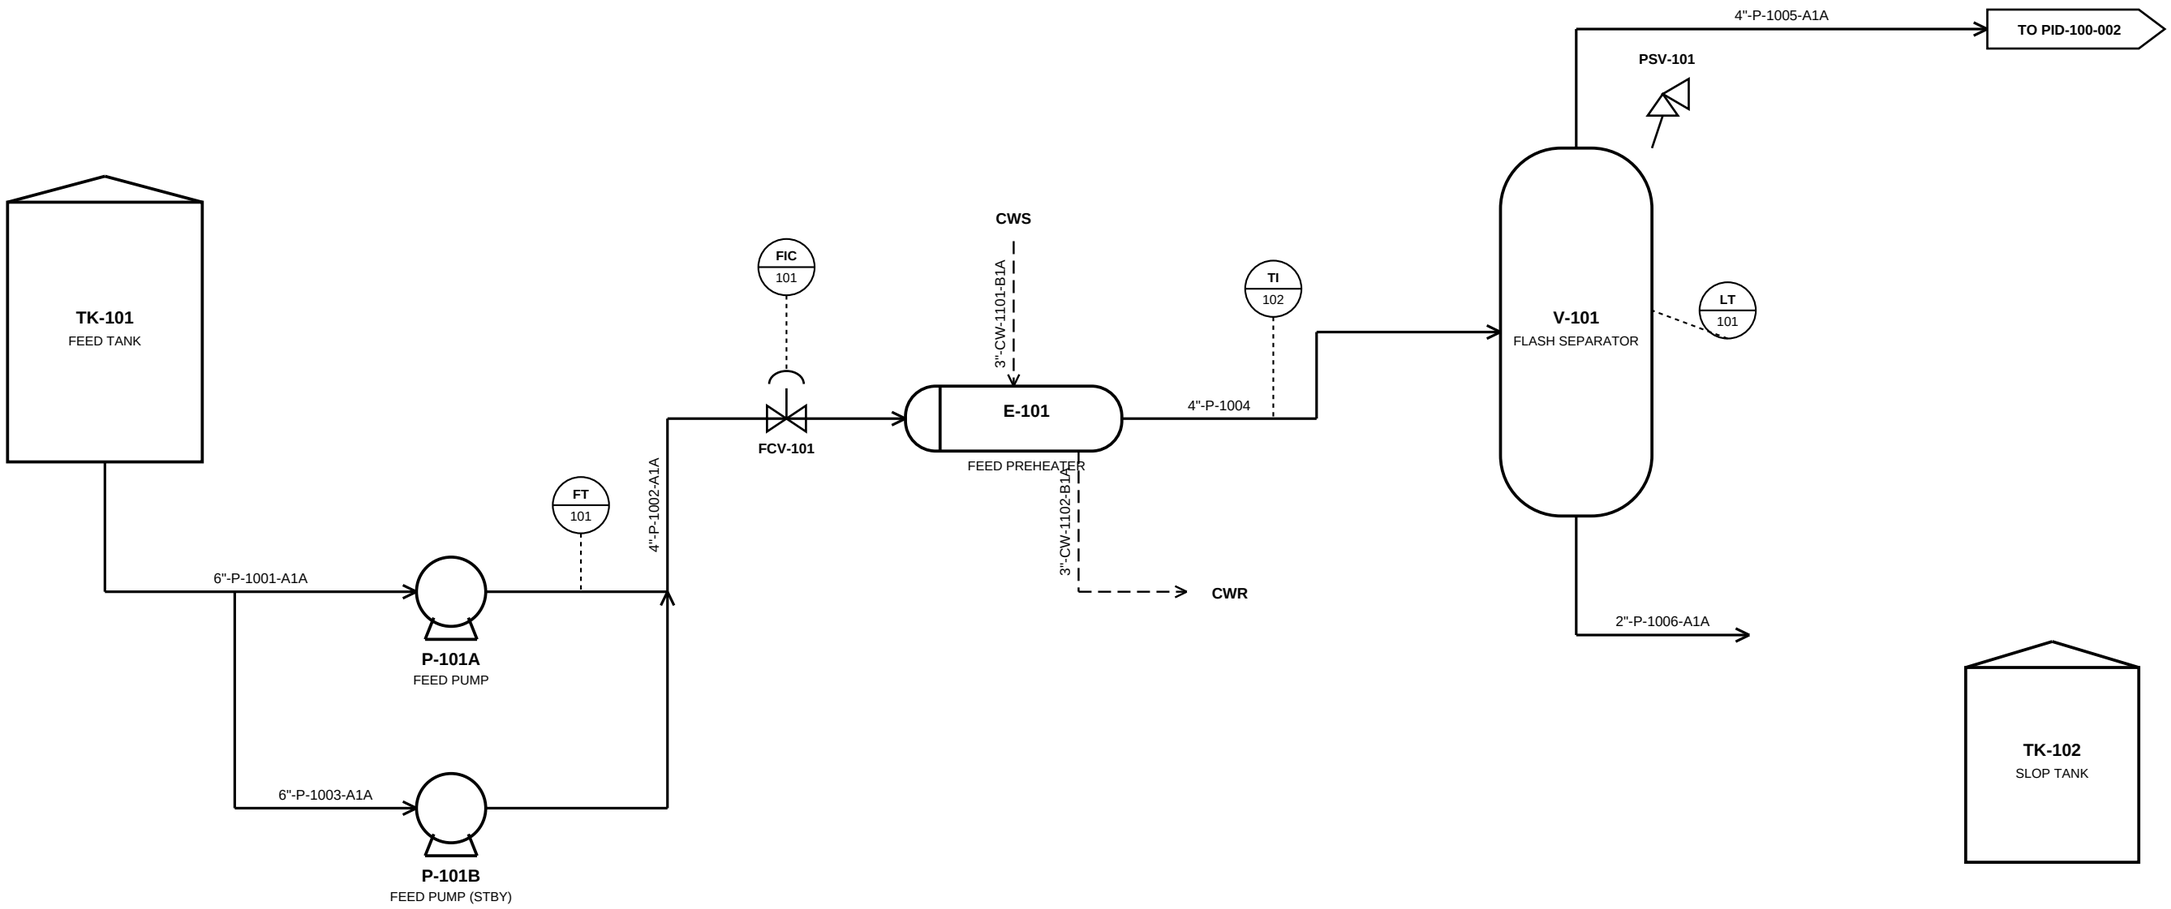


**FEED PREHEAT AND SEPARATION**
PIPING AND INSTRUMENT DIAGRAM - SAMPLE PROJECT

| DWG NO. | REV. |
|---|---|
| **PID-100-001** | **0** |